


Пеовый этаж (1:100)

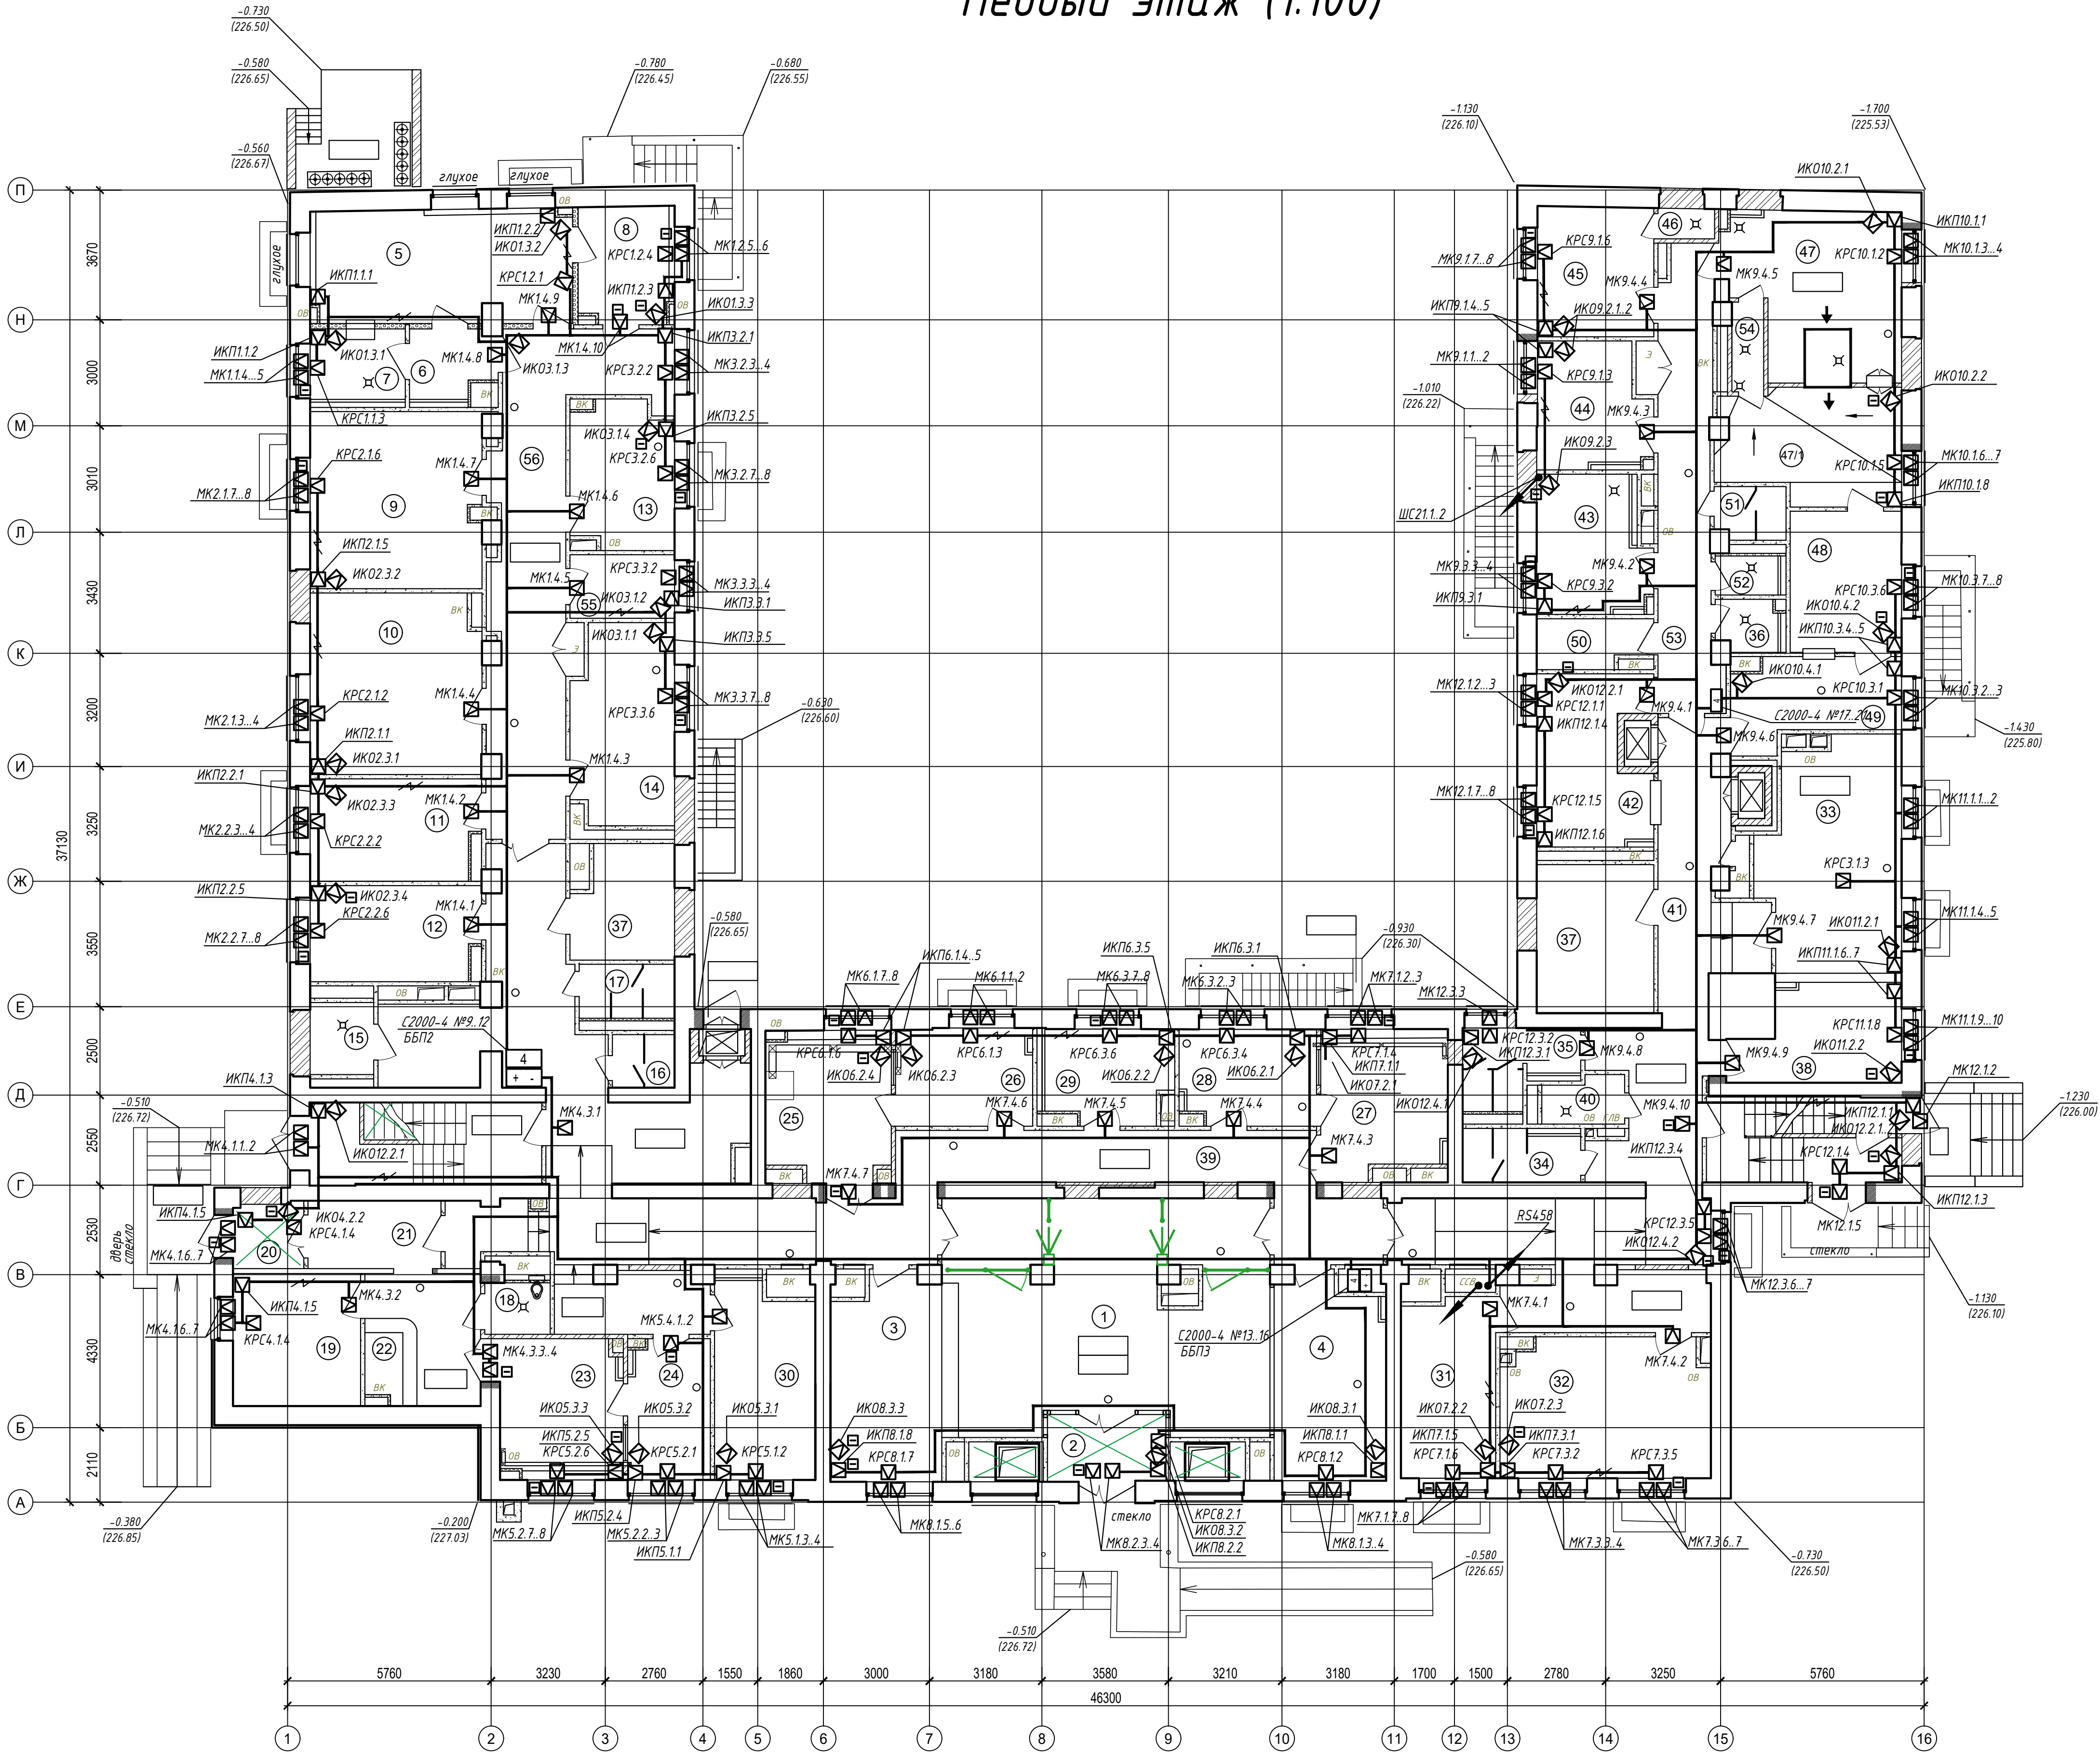

Экспликация помещений

Номер помещения	Наименование	Площадь м²
1	Вестибиль	59.50
2	Тамбур	6.20
3	Гардероб посетителей	17.60
4	Регистратура	17.60
5	Малая стоматологическая операционная	23.60
6	Предоперационная	4.80
7	Стерилизационная	6.00
8	Комната временного пребывания больных после операции	9.00
9	Стоматологический хирургический кабинет (2 места)	24.20
10	Стоматологический хирургический кабинет (2 места)	24.60
11	Стоматологический хирургический кабинет (1 место)	13.60
12	Стоматологический хирургический кабинет (1 место)	12.70
13	Стоматологический кабинет терапевтический (1 раб. место)	12.10
14	Стоматологический кабинет терапевтический для ФДП (1 раб. место)	15.80
15	Санузел инвалидов	3.70
16	Санузел персонала (женский)	2.60
17	Санузел персонала (мужской)	4.10
18	Санузел инвалидов	2.70
19	Стоматологический кабинет для инфекционных больных	13.20
20	Тамбур	2.90
21	Коридор	18.20
22	Гардероб посетителей	3.40
23	Процедурная рентгенографии с дентальным аппаратом	13.50
24	Комната управления	9.20
25	Процедурная К/КТ	14.30
26	Комната управления	10.70
27	Процедурная рентгенографии с дентальным аппаратом	14.40
28	Комната управления	10.30
29	Кабинет рентгенолога	9.70
30	Кабинет симуляционного оборудования	15.50
31	Кабинет цифровых технологий	13.40
32	Стоматологический кабинет терапевтический (2 раб. места)	22.60
33	Стоматологический кабинет терапевтический (2 раб. места)	23.70
34	Санузел посетителей (мужской)	5.10
35	Санузел посетителей (женский)	6.40
37	Вытяжная вентиляция	7.60
38	Кабинет старшей медсестры	11.00
39	Коридор	101.70
40	Кладовая уборочного инвентаря	2.90
41	Коридор	57.80
55	КРУ	5.30
56	Коридор	28.20
ЦСО		
36	Кладовая уборочного инвентаря	2.90
42	Помещение приема и хранения нестерильных материалов	14.50
43	Помещение разборки, мытья и сушки	4.20
44	Комната комплектации и упаковки	10.90
45	Комната персонала	12.10
46	Душевая	1.40
47	Стерилизационная-автоклавная (нестерильная зона)	21.50
47/1	Стерилизационная-автоклавная (стерильная зона)	15.60
48	Комната хранения стерильного материала	12.60
49	Помещение выдачи стерильных материалов	10.60
50	Кладовая упаковочных материалов	4.30
51	Санузел	3.00
52	Кладовая уборочного инвентаря	2.20
53	Коридор	20.30
54	Санпропускник	2.40

Условно-графические обозначения

№	Обозначение	Наименование
1	ИЗ	Извещатель звуковой GBD-R-1
2	ИЗ	Извещатель объемный ИИС-105
3	ИЗ	Извещатель магнитоконтактный
4	ИЗ	Извещатель поверхностный ИИС-106
5	УО	Устройство оконечное
6	Ш	Шлейф сигнальный охранный

				ГУИР 425118.015 36				
Изм	Лист	№ докум.	Подп.	Дата	Система охранной сигнализации Схема электрическая общая	Лит.	Масса	Масштаб
Разраб.	Каширский					Т		
Проб.	Алефиренко							
Т.контр.	Алефиренко							
Реч.	Асениченко							
Н.контр.	Калита					Лист	Листов 1	
Утв.	Ячин					ПИКС, гр. 113301		