


Первый этаж (1:100)

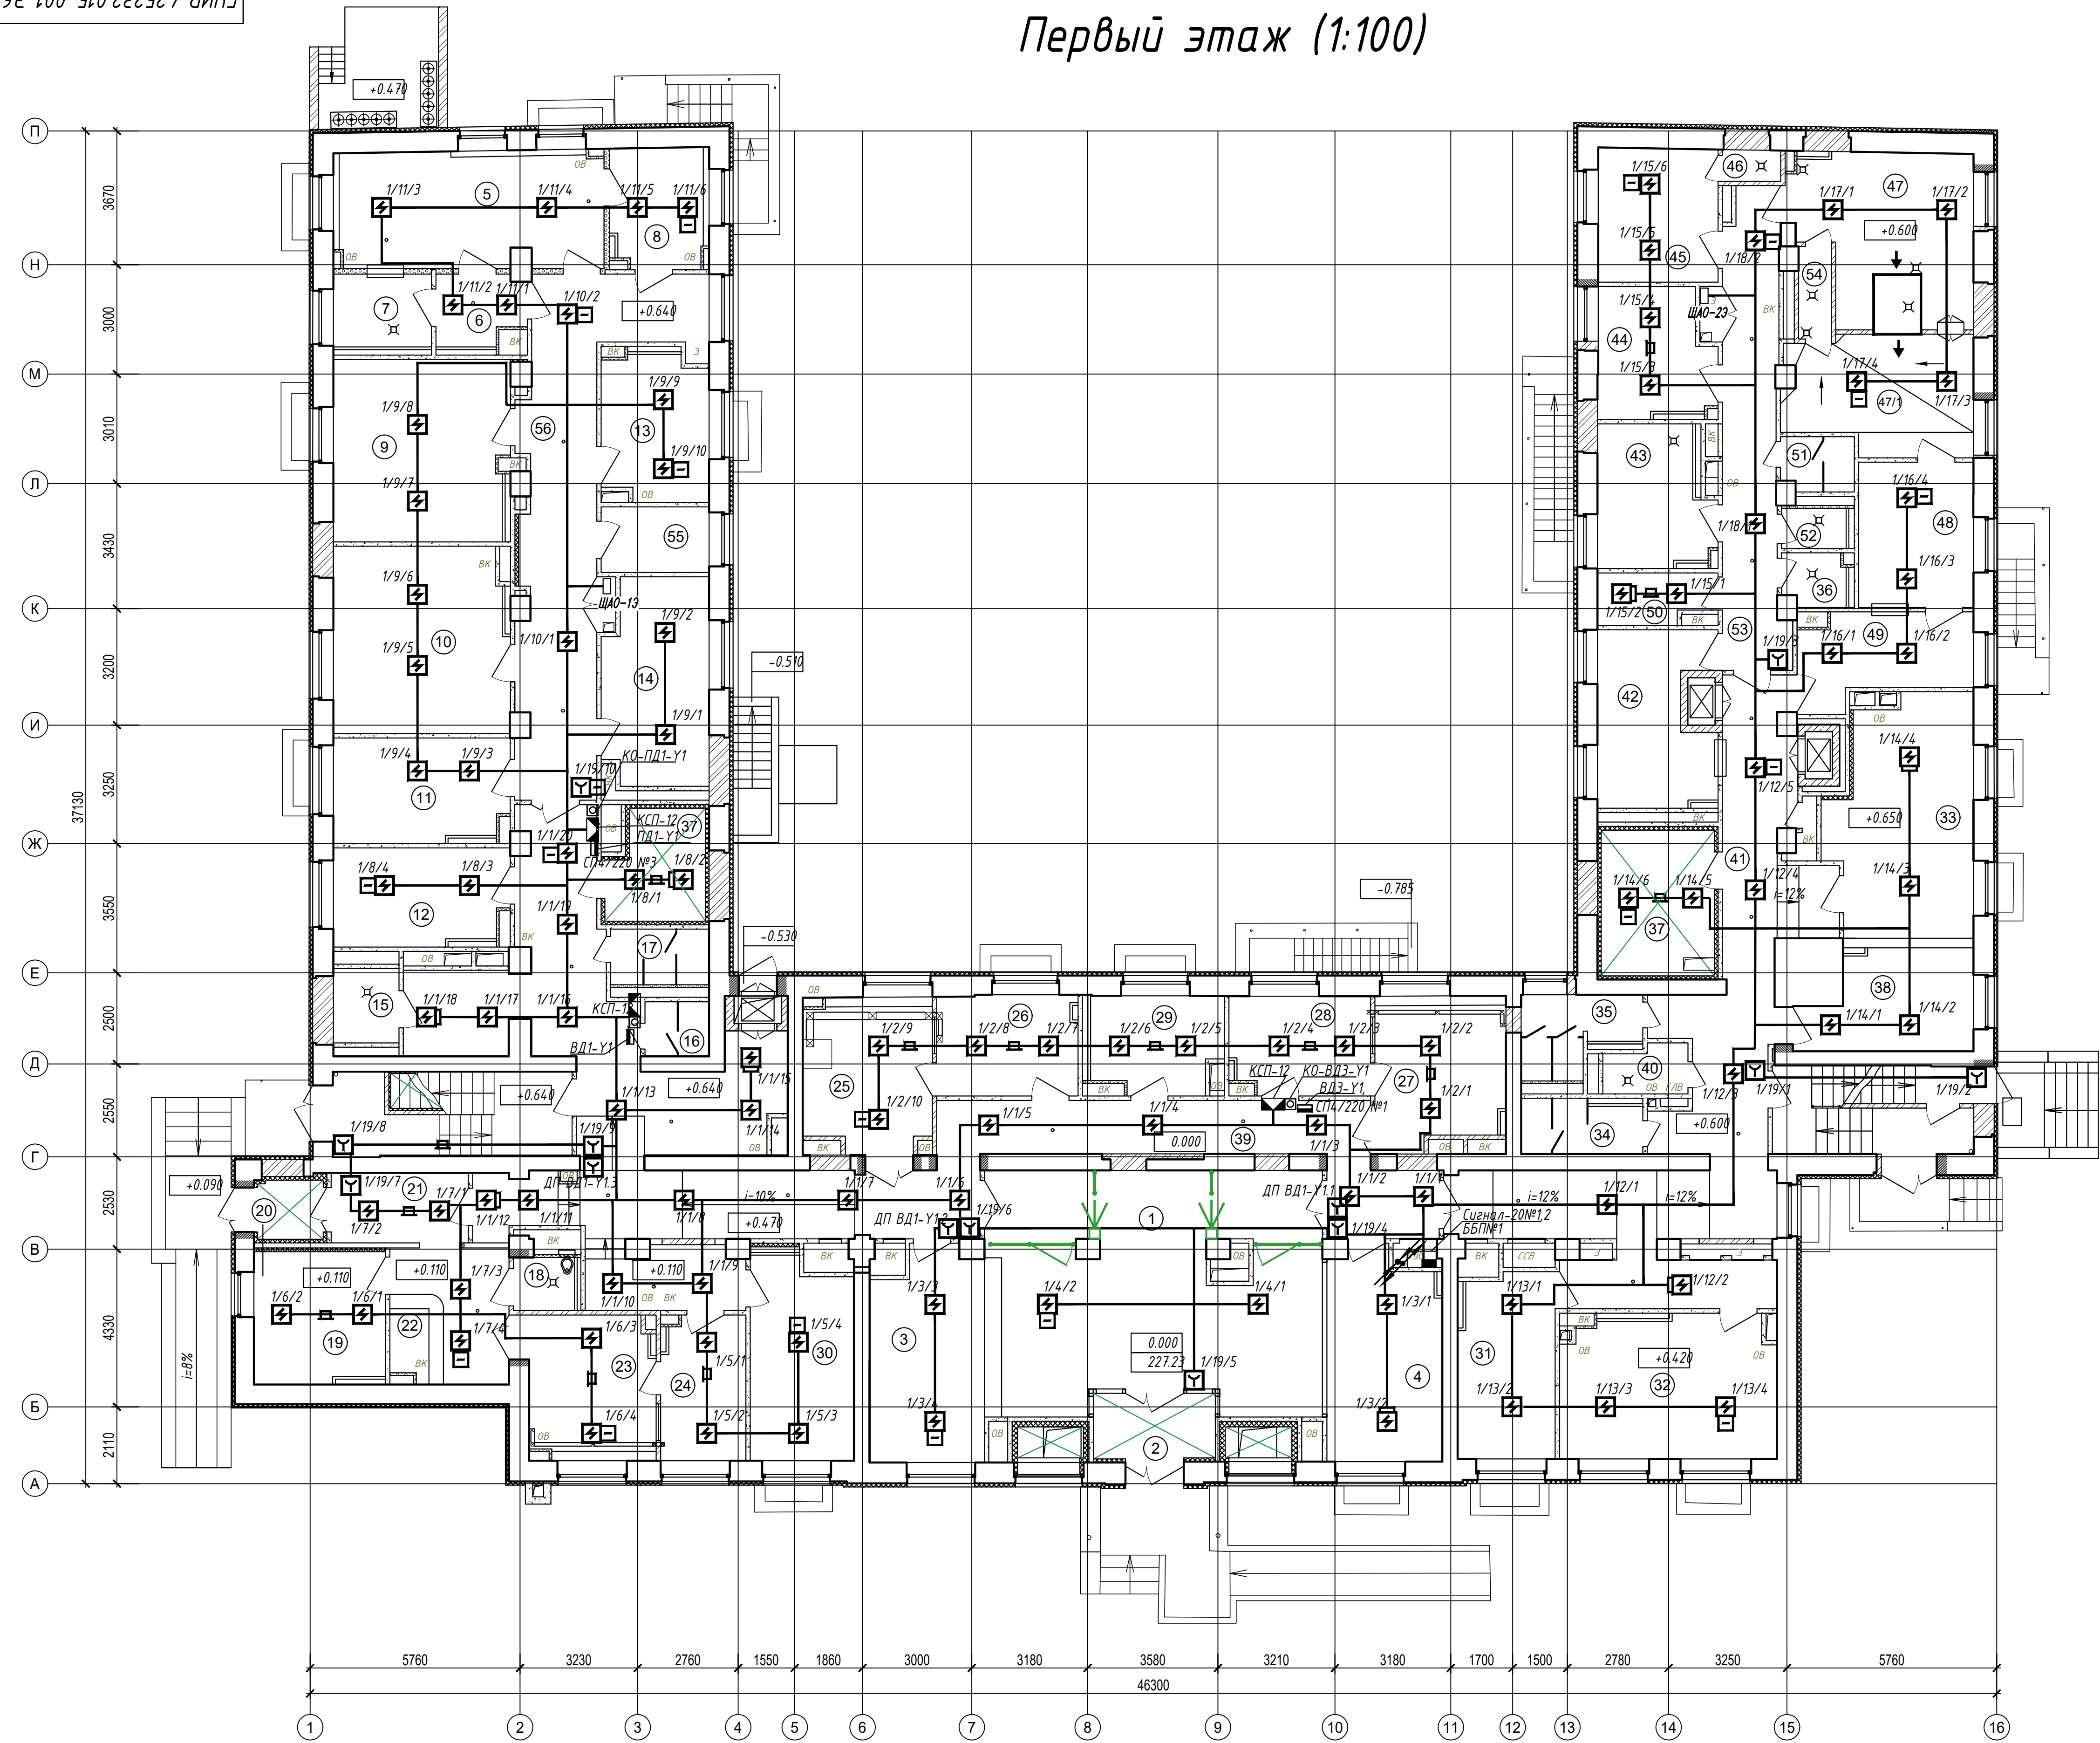

Экспликация помещений

Номер помещения	Наименование	Площадь м²
1	Вестибаль	59.50
2	Тамбур	6.20
3	Гардероб посетителей	17.60
4	Регистратура	17.60
5	Малая стоматологическая операционная	23.60
6	Предоперационная	4.80
7	Стерилизационная	6.00
8	Комната временного пребывания больных после операции	9.00
9	Стоматологический хирургический кабинет (2 места)	24.20
10	Стоматологический хирургический кабинет (2 места)	24.60
11	Стоматологический хирургический кабинет (1 место)	13.60
12	Стоматологический хирургический кабинет (1 место)	12.70
13	Стоматологический кабинет терапевтический (1 раб. место)	11.60
14	Стоматологический кабинет терапевтический для ФОП (1 раб. место)	15.80
15	Санузел инвалидов	3.70
16	Санузел персонала (женский)	2.60
17	Санузел персонала (мужской)	4.10
18	Санузел инвалидов	2.70
19	Стоматологический кабинет для инфекционных больных	13.20
20	Тамбур	2.90
21	Коридор	18.20
22	Гардероб посетителей	3.40
23	Процедурная рентгенографии с дентальным аппаратом	13.50
24	Комната управления	9.20
25	Процедурная К/КТ	14.30
26	Комната управления	10.70
27	Процедурная рентгенографии с дентальным аппаратом	14.40
28	Комната управления	10.30
29	Кабинет рентгенолога	9.70
30	Кабинет симуляционного оборудования	15.50
31	Кабинет цифровых технологий	13.40
32	Стоматологический кабинет терапевтический (2 раб. места)	22.60
33	Стоматологический кабинет терапевтический (2 раб. места)	23.70
34	Санузел посетителей (мужской)	5.10
35	Санузел посетителей (женский)	6.40
37	Вытяжная вентиляция	7.60 12.40
38	Кабинет старшей медсестры	11.90
39	Коридор	97.90
40	Кладовая уборочного инвентаря	2.90
41	Коридор	57.80
55	КРУ	5.30
56	Коридор	35.40
ЦСО		
36	Кладовая уборочного инвентаря	2.90
42	Помещение приема и хранения нестерильных материалов	14.50
43	Помещение разборки, мытья и сушки	12.20
44	Комната комплектации и упаковки	10.90
45	Комната персонала	12.10
46	Душевая	1.40
47	Стерилизационная-автоклавная (стерильная зона)	21.50
47/1	Стерилизационная-автоклавная (стерильная зона)	15.60
48	Комната хранения стерильного материала	12.60
49	Помещение выдачи стерильных материалов	10.60
50	Кладовая упаковочных материалов	4.30
51	Санузел	3.00
52	Кладовая уборочного инвентаря	2.20
53	Коридор	20.30
54	Санпропускник	2.40

Условно-графические обозначения

№	Обозначение	Наименование
1		Дымовой ПИ ИП212-5МУ
2		Ручной ПИ ИПР 5-2Р
3		Устройство оконечное
4		Шлейф сигнальный в лотке

ГУИР 425232.015-001 36				Система пожарной сигнализации			Лит.	Масса	Масштаб
Изм.	Лист	№ докум.	Подп.	Дата	Схема электрическая общая			Т	
Разраб.	Алефиренко								
Проб.	Алефиренко								
Т.контр.	Асценко							Лист	Листов 1
Рец.	Асценко				Пикс, гр. 113301			Формат А1	
Н.контр.	Калита								
Утв.	Ячин				Копировал				