


Второй этаж (1:100)

Экспликация помещений

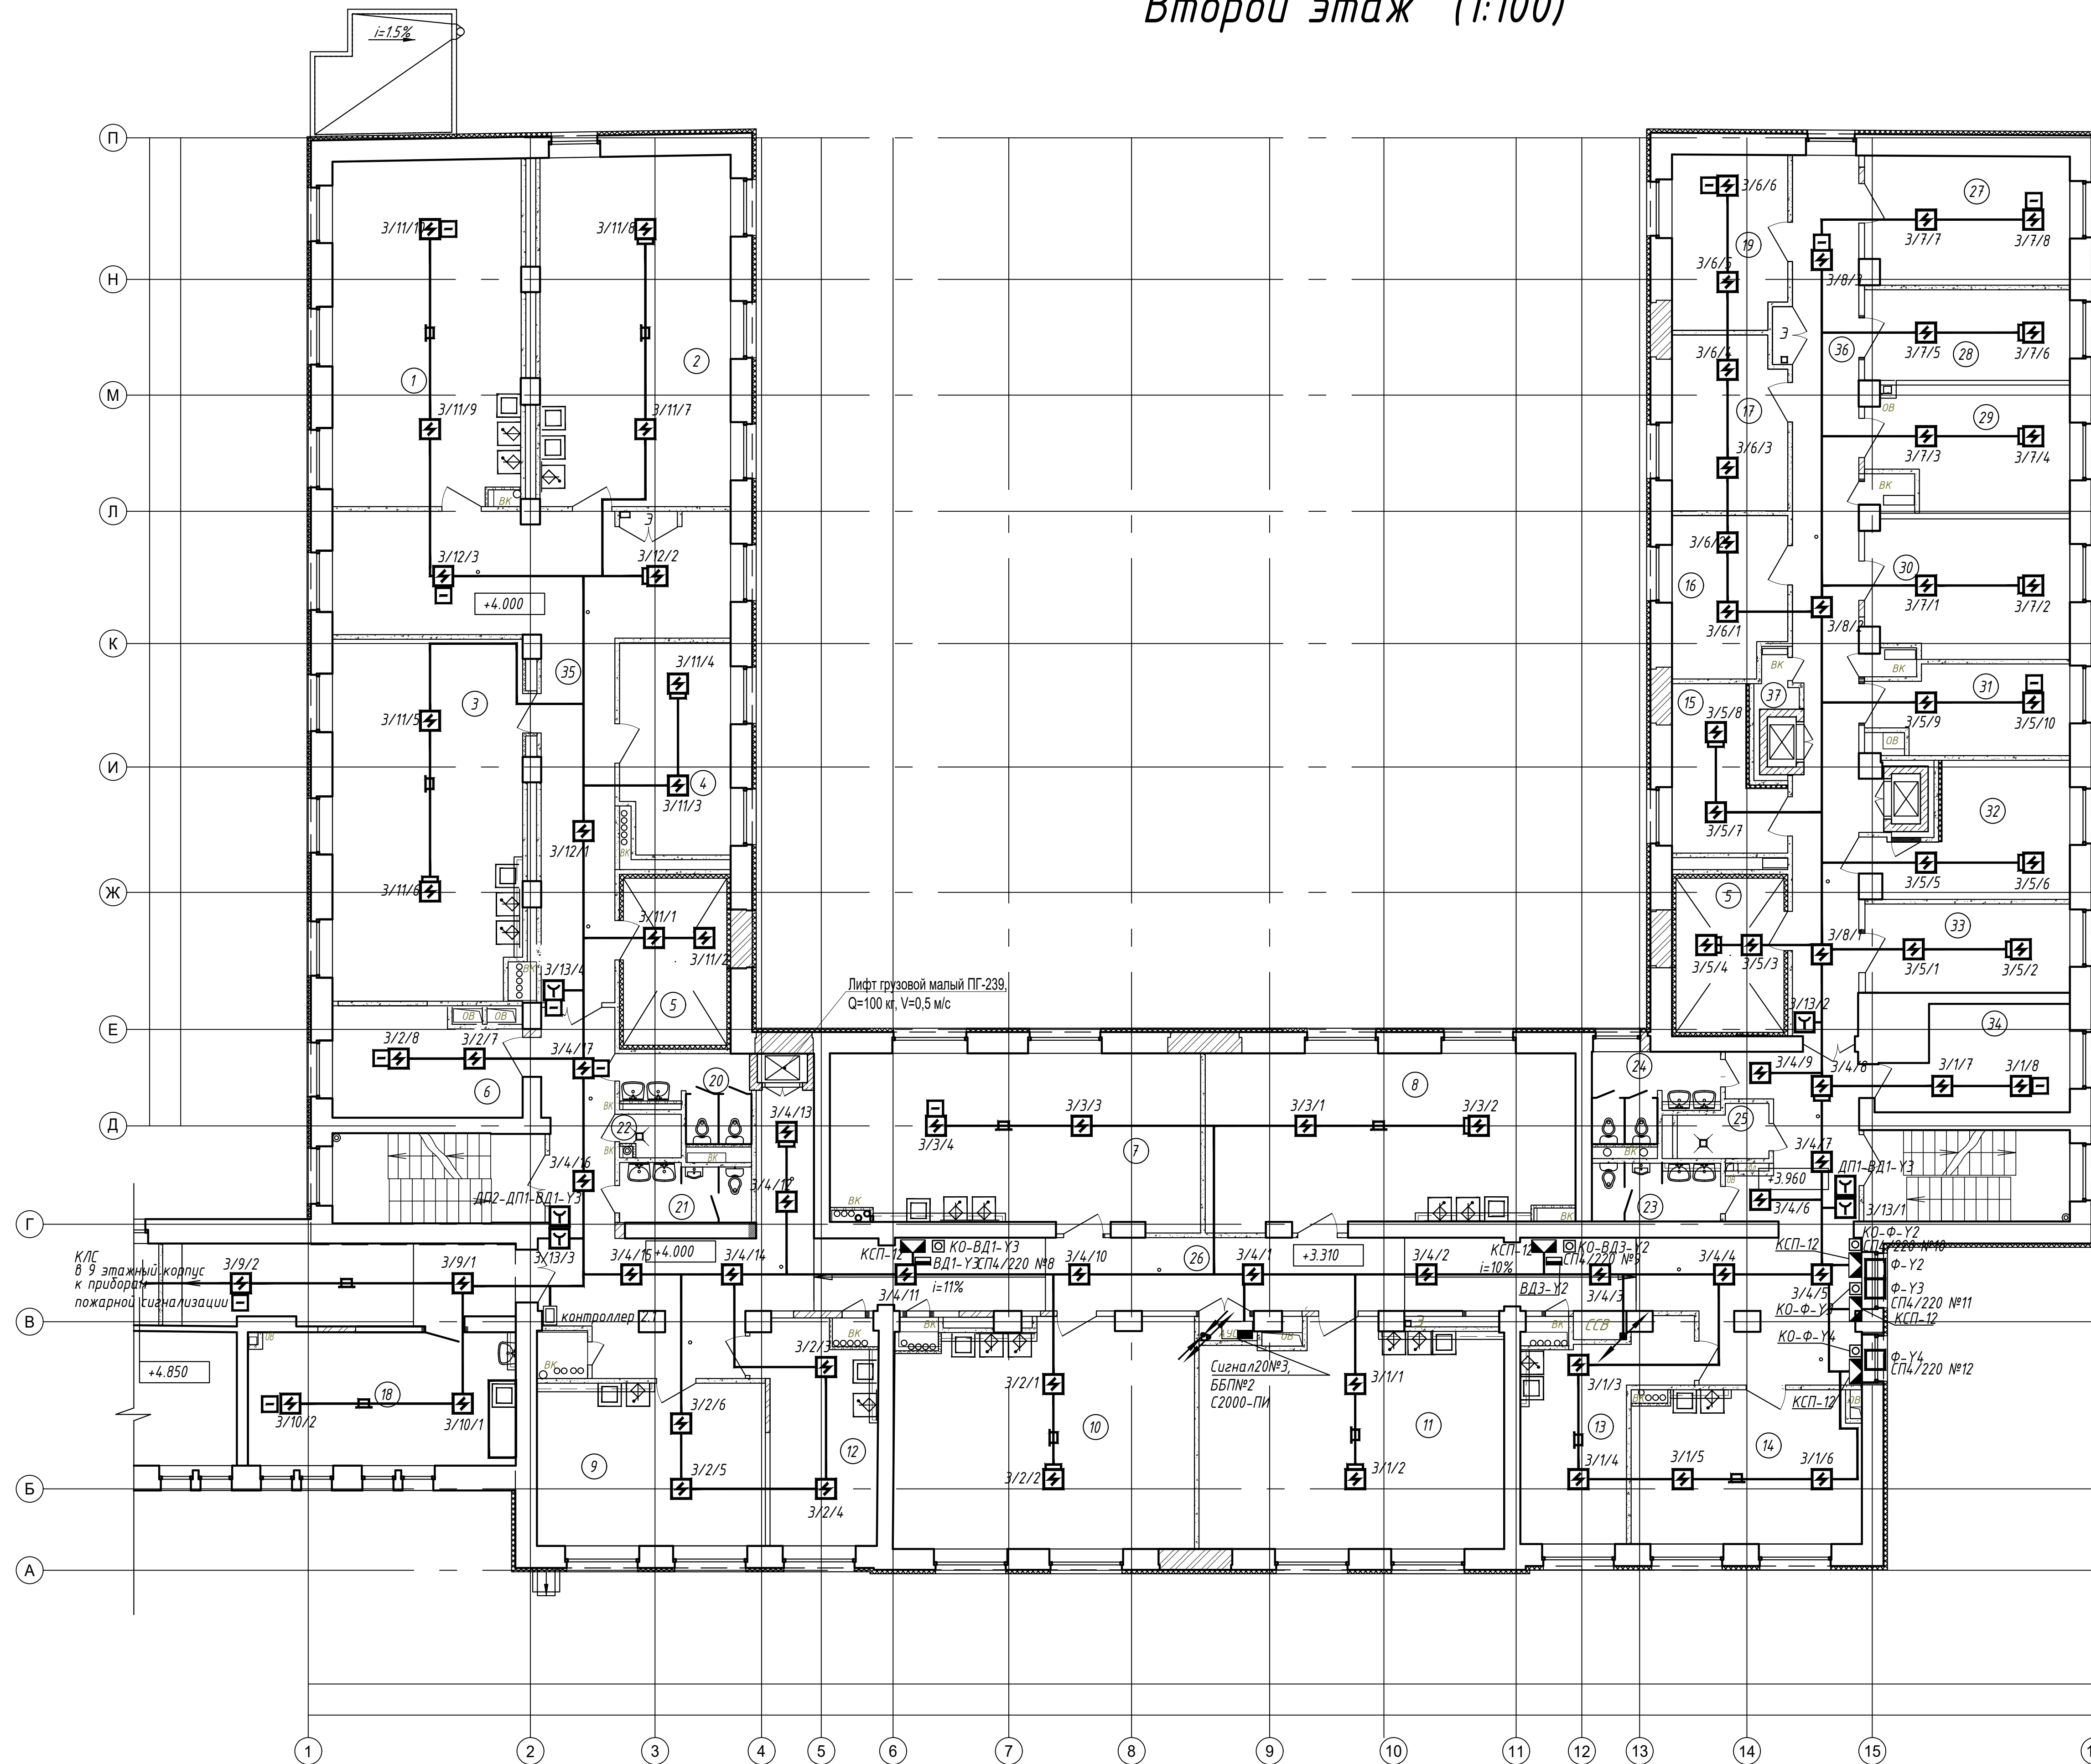

Номер помещения	Наименование	Площадь м ²
1	Стоматологический кабинет для проведения учебных занятий (4 стоматологических комплекса)	43.41
2	Стоматологический кабинет для проведения учебных занятий (4 стоматологических комплекса)	44.82
3	Стоматологический кабинет для проведения учебных занятий (4 стоматологических комплекса)	44.78
4	Кабинет профессорско-преподавательского состава (2 чел.)	15.32
5	Вытяжная вентиляция	11.20x2
6	Кабинет профессорско-преподавательского состава (2 чел.)	13.03
7	Стоматологический кабинет (3 стоматологических комплекса)	42.44
8	Стоматологический кабинет (3 стоматологических комплекса)	42.27
9	Стоматологический кабинет (2 стоматологических комплекса)	24.90
10	Стоматологический кабинет (3 стоматологических комплекса)	44.52
11	Стоматологический кабинет (3 стоматологических комплекса)	45.03
12	Стоматологический кабинет (1 стоматологический комплекс)	16.09
13	Стоматологический кабинет (1 стоматологический комплекс)	16.88
14	Стоматологический кабинет (2 стоматологических комплекса)	23.06
15	Кабинет зам.главного врача по ОМО (1чел.)	10,18
16	Кабинет зам.главного врача по хозяйственной работе (1 чел.)	11.60
17	Оргметодкабинет (2 чел.)	13.27
18	Комната приема пищи	24.00
19	Кабинет медицинской статистики (2 чел.)	13.22
20	Санузел персонала (женский)	6.05
21	Санузел персонала (мужской)	5.11
22	Кладовая уборочного инвентаря	1.64
23	Санузел посетителей (мужской)	5.04
24	Санузел посетителей (женский)	6.50
25	Кладовая уборочного инвентаря	3,27
26	Коридор	112,61
27	Комната инженеров (3 чел.)	17.53
28	Кабинет главного бухгалтера (1чел.)	12.50
29	Бухгалтерия (3чел.)	15.67
30	Бухгалтерия (3чел.)	18.45
31	Кабинет экономистов (2 чел.)	11.14
32	Комната юриконсульта, специалиста по закупкам, программиста (3чел.)	14.72
33	Комната администрации (2 чел.)	12.19
34	Кабинет отдела кадров	12.05
35	Коридор	50,64
36	Коридор	38,35
37	Помещение прохода инженерных коммуникаций	1,79

Условно-графические обозначения

№	Обозначение	Наименование
1		Дымовой ПИ ИП212-5МУ
2		Ручной ПИ ИПР 5-2Р
3		Устройство оконечное
4		Шлейф сигнальный в лотке

[illegible]