
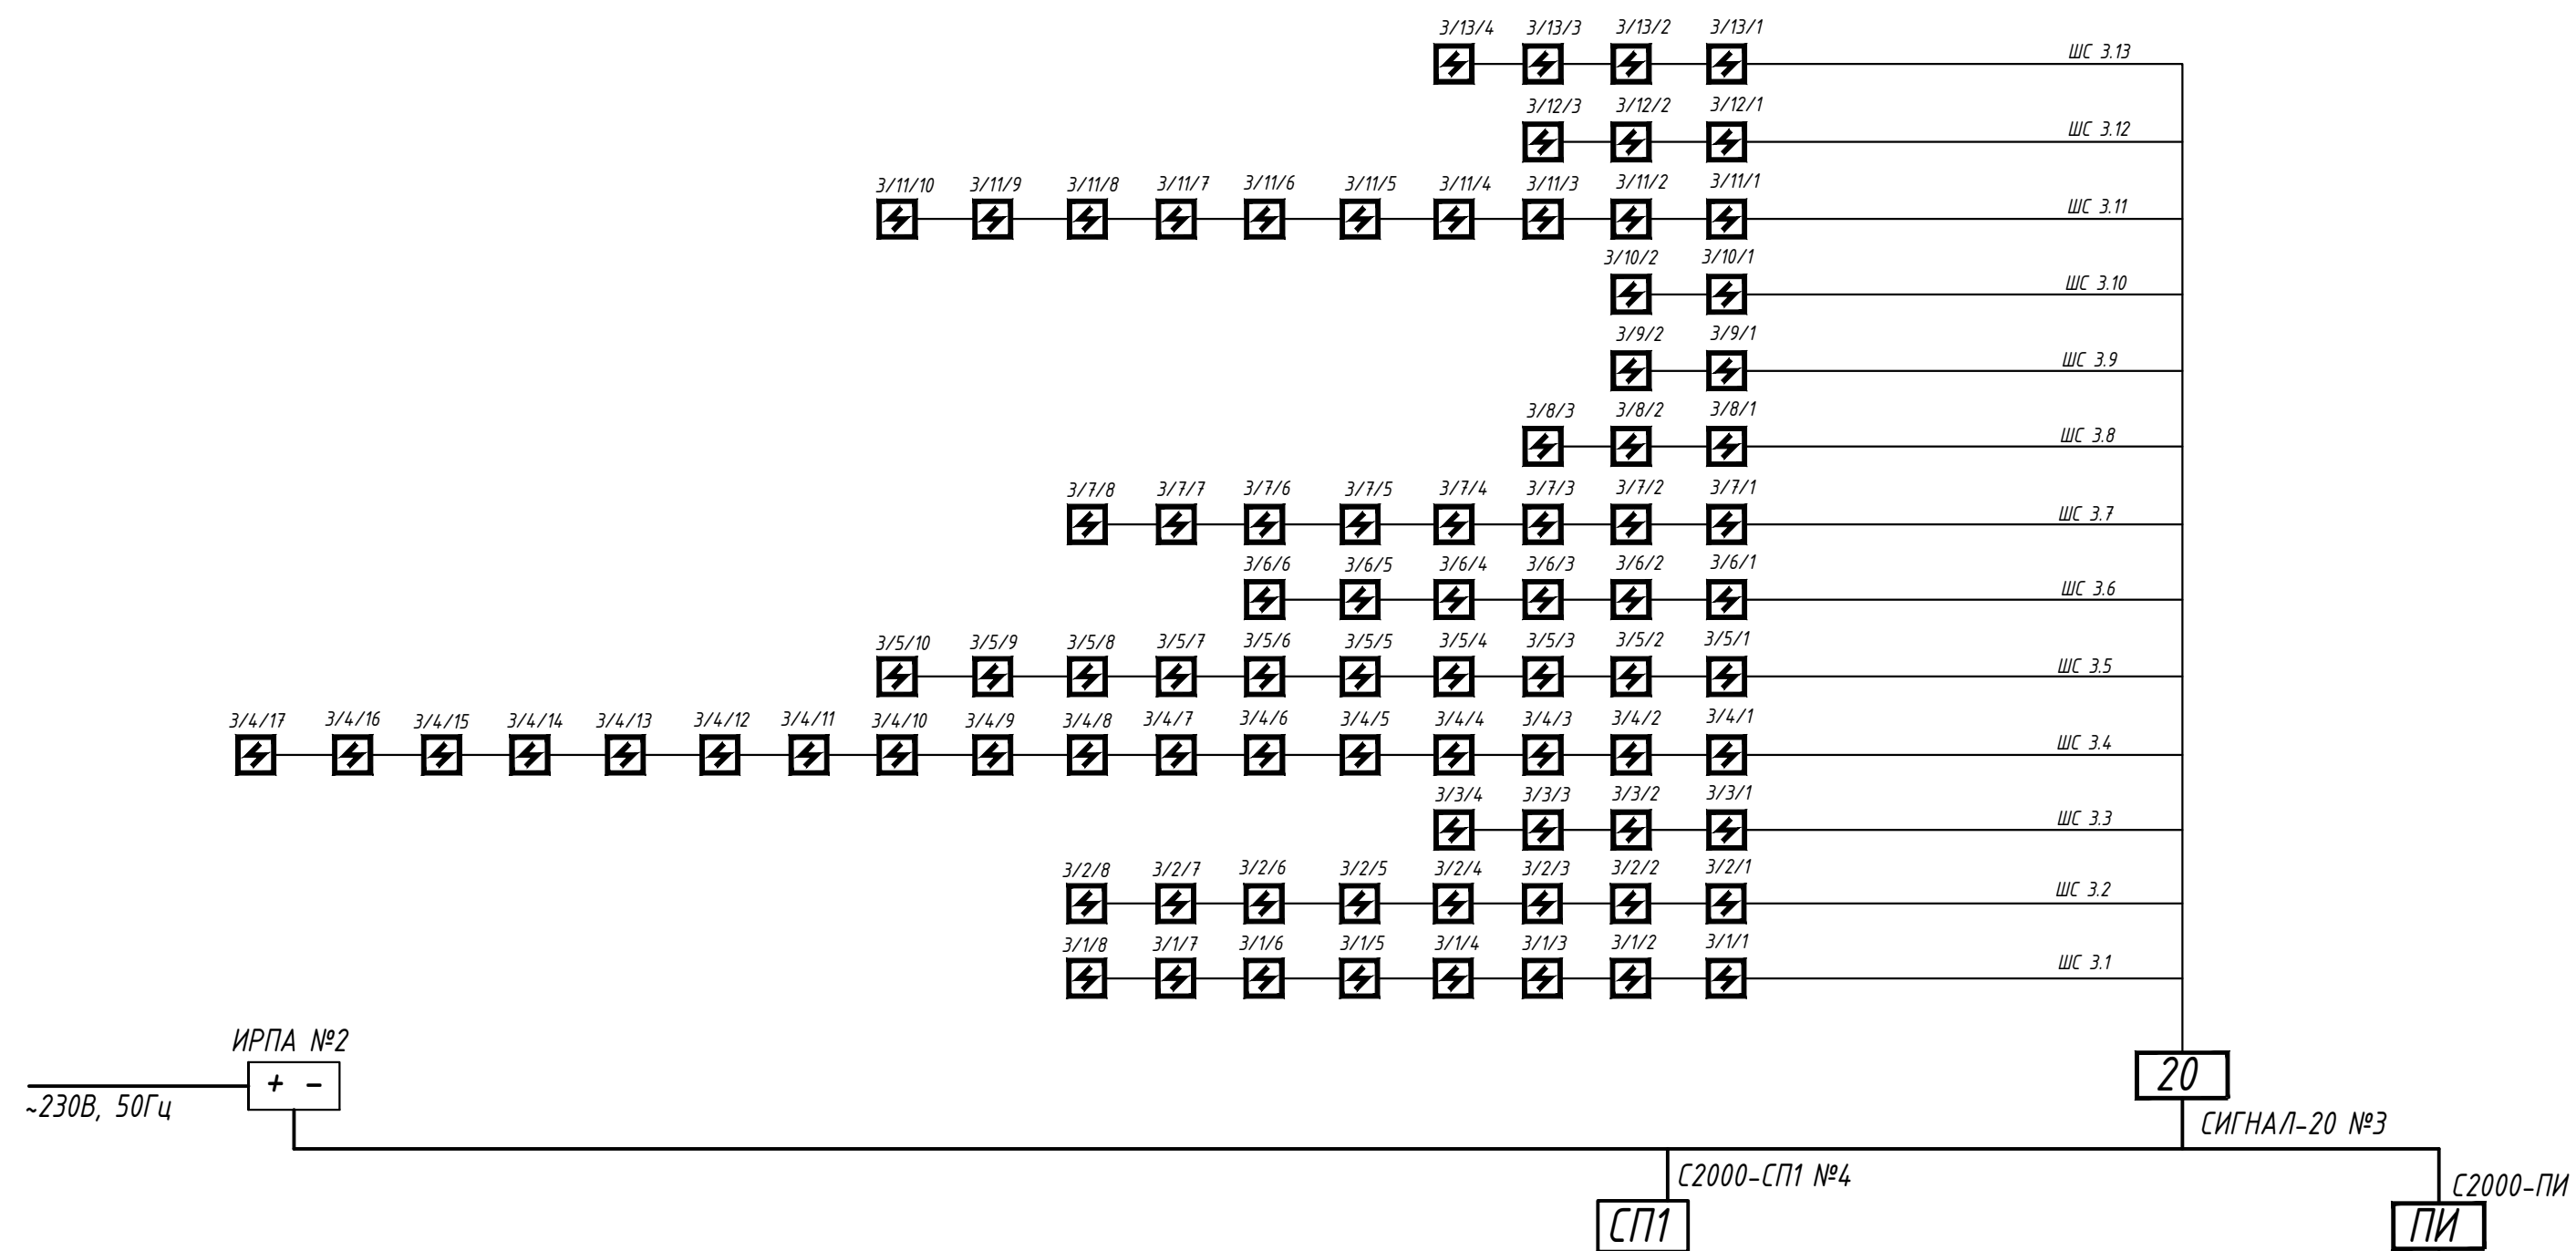


2 этаж

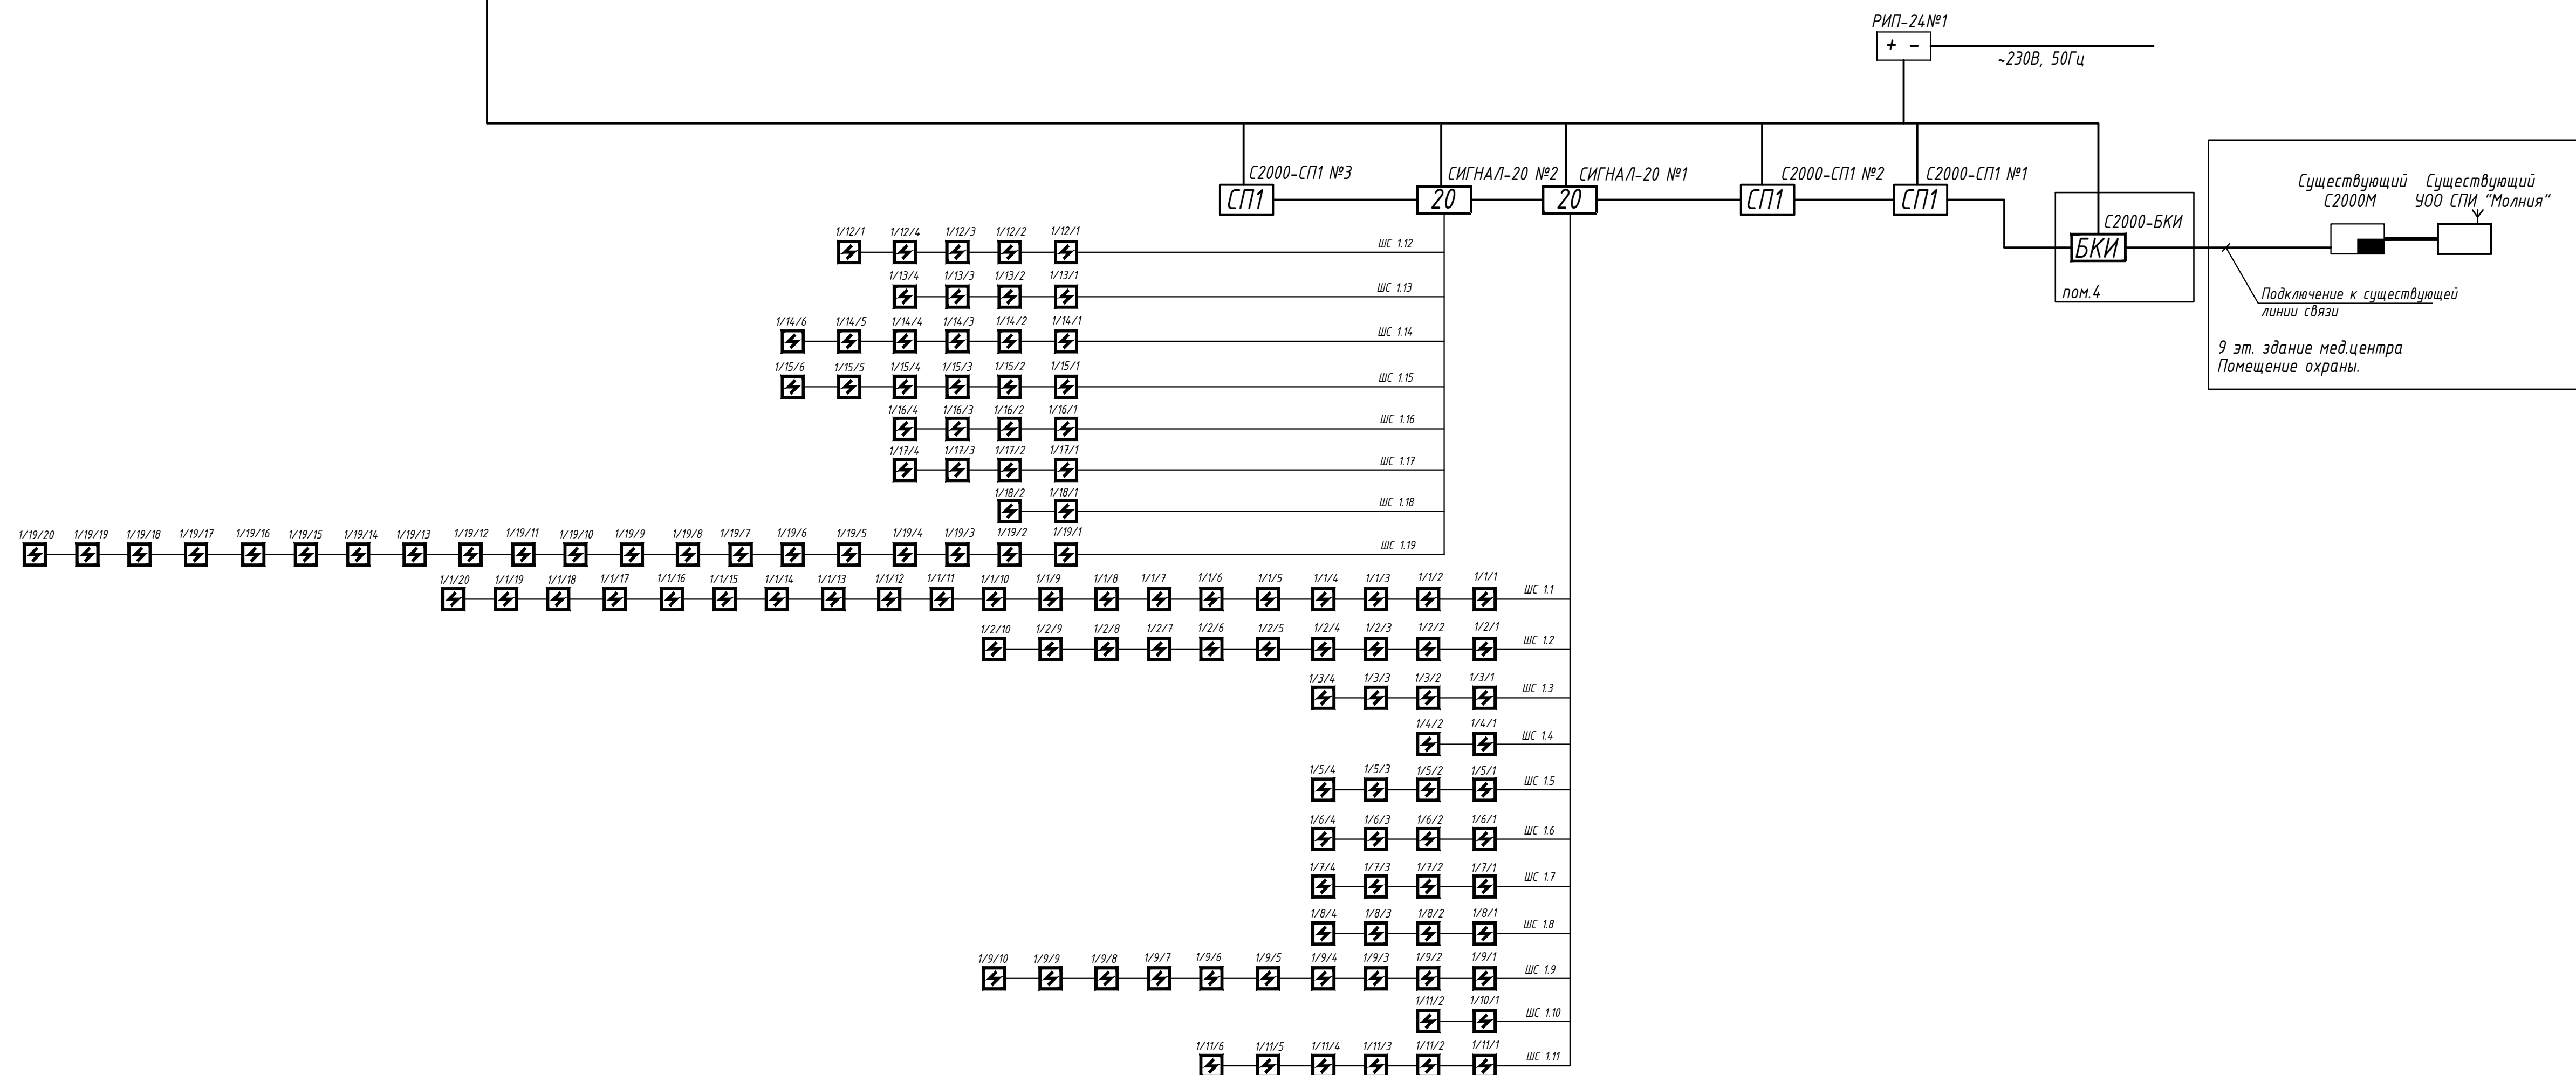

1 этаж

[illegible]